


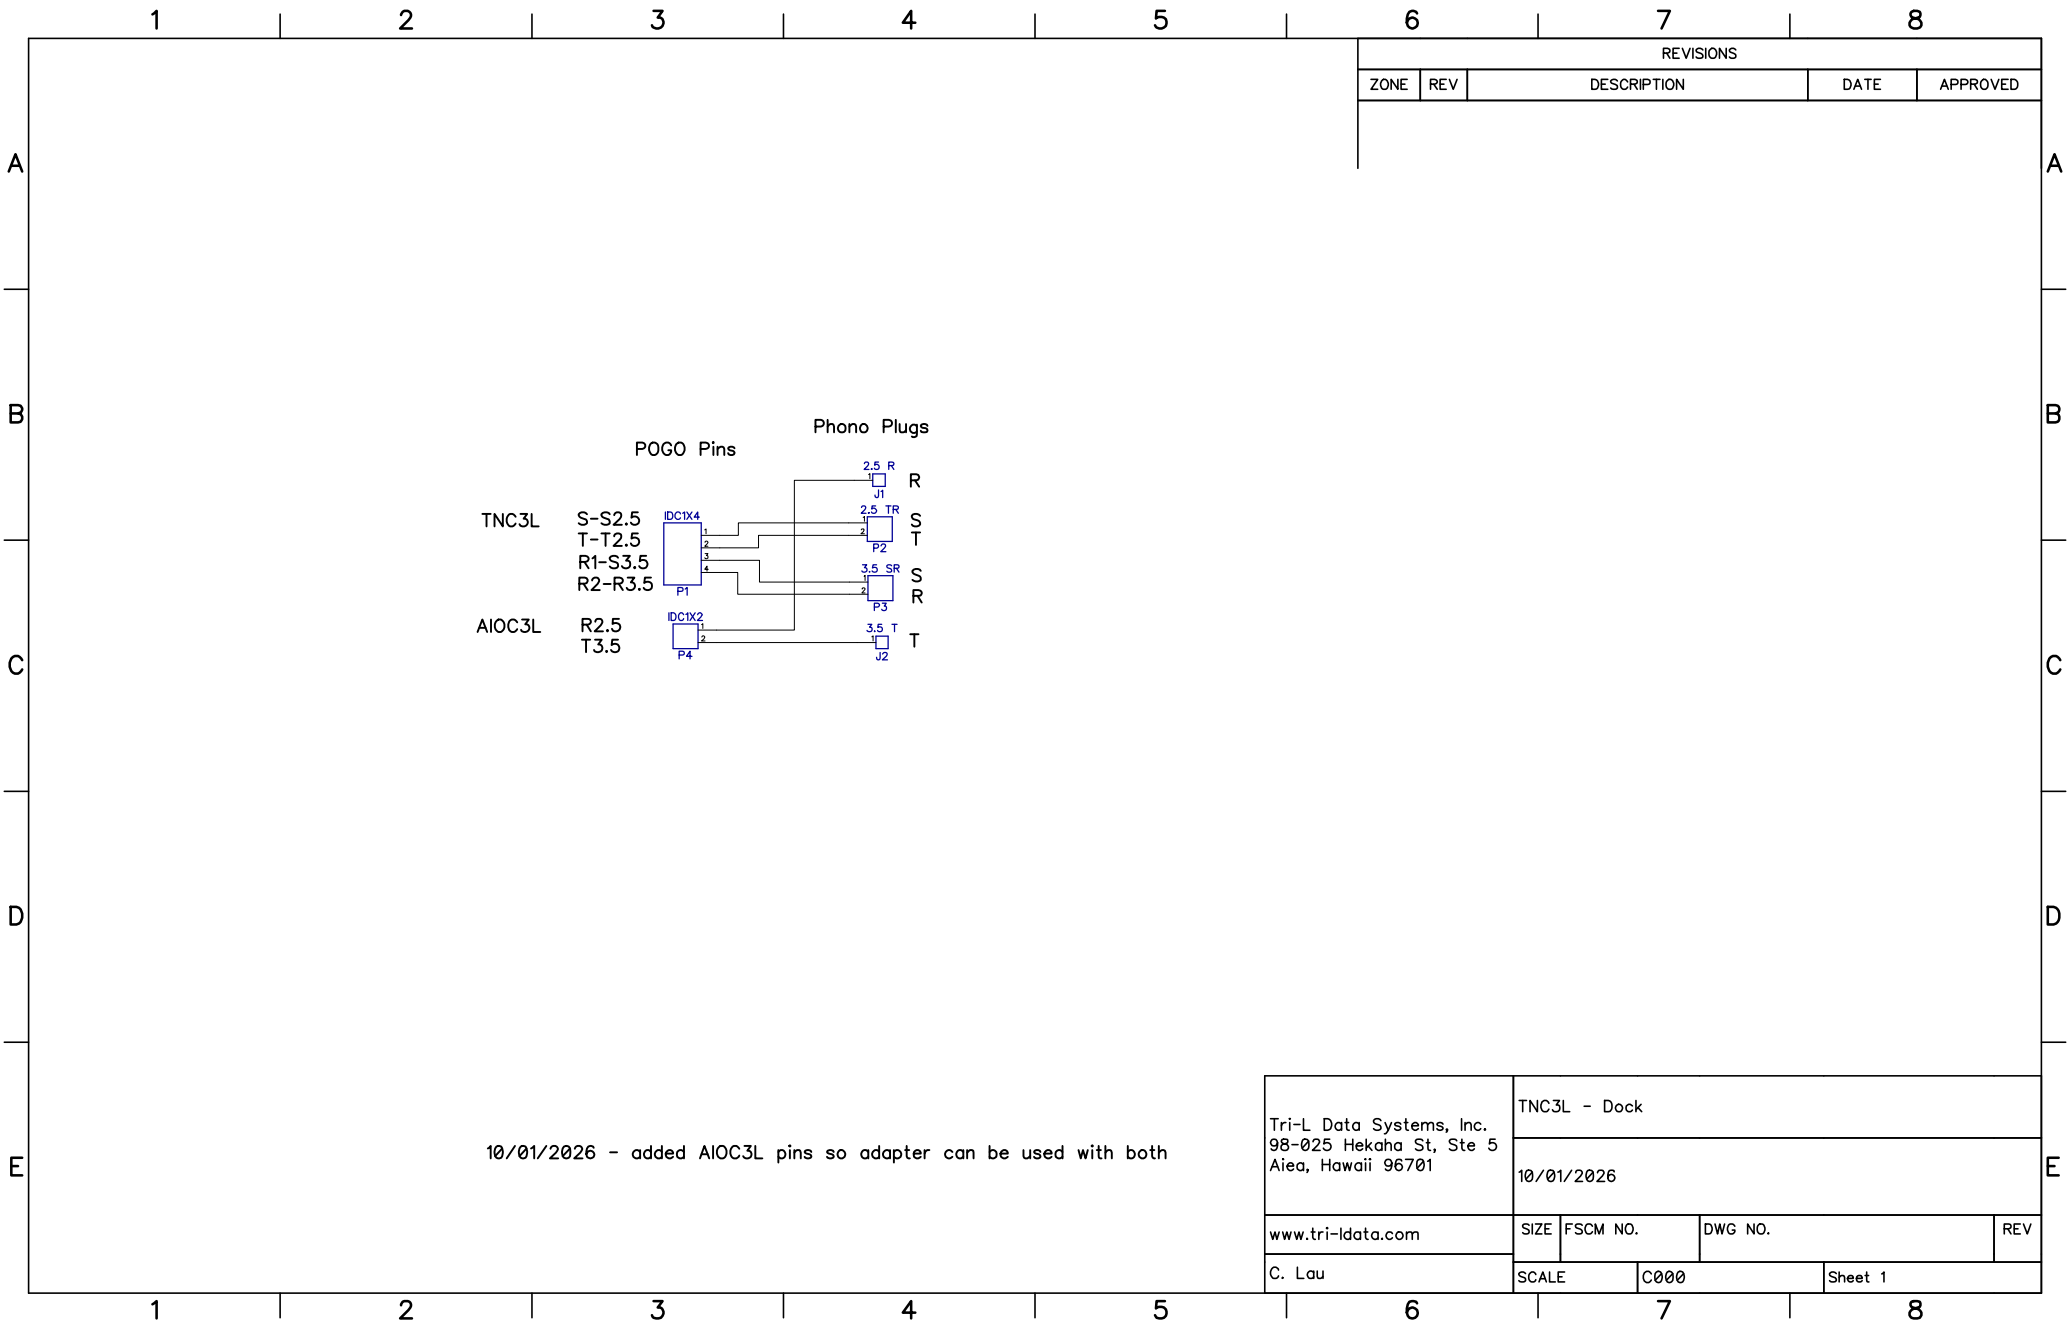

REVISIONS				
ZONE	REV	DESCRIPTION	DATE	APPROVED

Tri-L Data Systems, Inc. 98-025 Hekaha St, Ste 5 Aiea, Hawaii 96701	TNC3L - Dock			
	10/01/2026			
www.tri-ldata.com	SIZE	FSCM NO.	DWG NO.	REV
C. Lau	SCALE	C000	Sheet 1	